


کنسول 60 سانتیمتری
مجاز برای طبقه اول

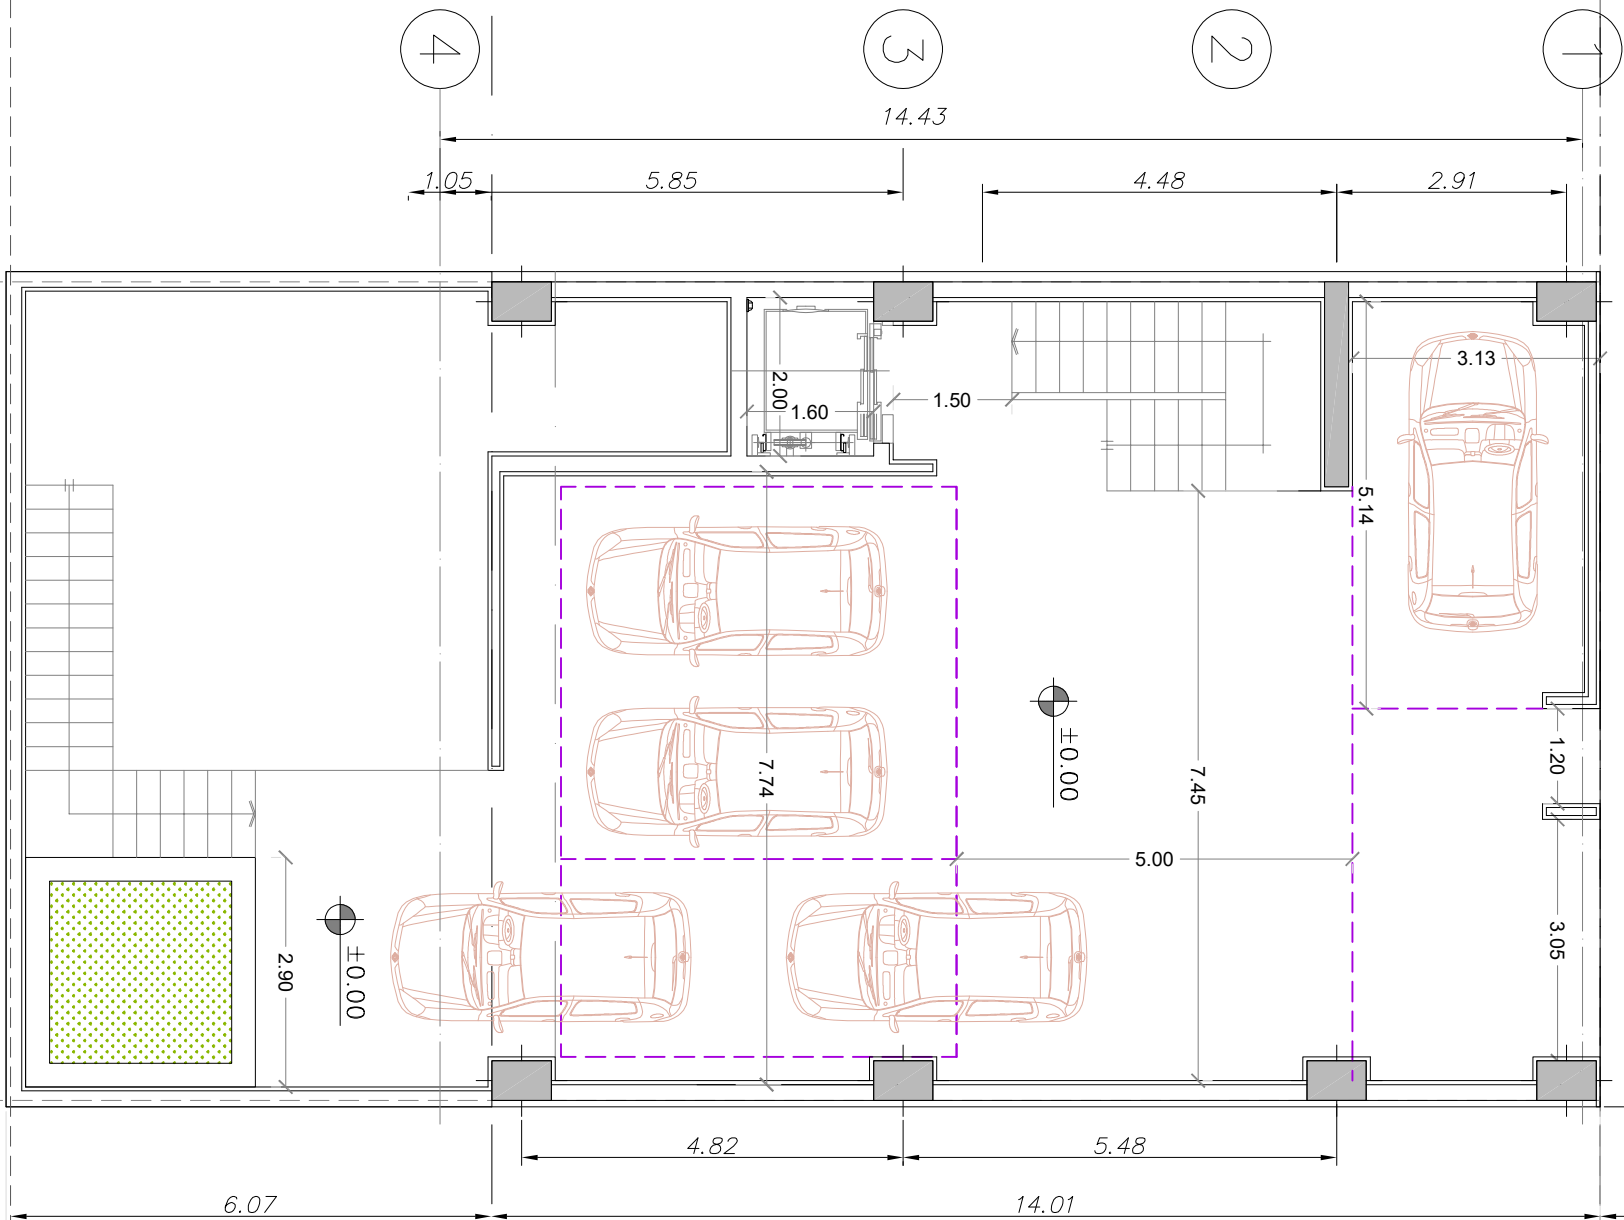

پیشروی مجاز ساختمان بر اساس
60 درصد به اضافه 2 متر

PROJECT NAME : **MR.S-KASHI`S-PROJECT**

DRAWING NAME : **GF-FLOOR-PLAN**

SCALE : **1/100** DATE : **1403/08/19**

SHEET_NUM : **A3_002**